

All rights reserved. No part of these drawings or specifications may be copied, reproduced or used in connection with any work, other than the specific project for which they have been prepared, without prior written authorization from the Architect.

STOREFRONT NOTES:

GENERAL NOTES:

- GC IS RESPONSIBLE FOR ENGINEERING STOREFRONT.
- SUBMIT COMPLETE SHOP DRAWINGS, TECHNICAL INFORMATION, & SAMPLES FOR ALL DOOR & SIDE LITE COMPONENTS.
- ALL DISSIMILAR METALS SHALL BE ISOLATED FROM ONE ANOTHER AS REQUIRED TO PREVENT GALVANIC CORROSION.
- ALL PLYWOOD AND BLOCKING SHALL BE EXTERIOR GRADE AND SUITABLE FOR WET LOCATIONS.

EXISTING STOREFRONT SYSTEM

- ALL EXISTING WINDOW FRAMING TO BE CLAD IN MT-2. SEE FINISH SCHEDULE FOR MORE INFORMATION.

GLASS DOORS & SIDE LITES

- COMPLETE SHOP DRAWINGS SHALL BE SUBMITTED WITHIN THREE WEEKS OF AWARD CONTRACT.
- ALL EXPOSED SHALL BE SHOP FINISHED & POWDER COATED TO MATCH MT-2. SEE FINISH SCHEDULE FOR MORE INFORMATION.
- GLASS SHALL BE GL-2. SEE FINISH SCHEDULE FOR MORE INFORMATION.
- NO VISIBLE FASTENERS ALLOWED.
- UNLESS OTHERWISE NOTED, SEALANTS AT THE PERIMETER OF STOREFRONT ELEMENTS SHALL BE RECESSED AND MATCH THE COLOR OF SURROUNDING MATERIALS.
- G.C. TO PROVIDE 1" HIGH SIGN ON EGRESS SIDE BOTTOM DOOR RAIL: **THIS DOOR TO REMAIN UNLOCKED WHEN SPACE IS OCCUPIED**

ELECTROSTATIC PAINT NOTES:

- SCOPE: ELECTROSTATIC PAINTING WILL ONLY OCCUR AT THE EXISTING STOREFRONT FRAMING.
- ELECTROSTATIC PAINTING MUST BE DONE BY A SUBCONTRACTOR SPECIALIZING IN SUCH WORK. SUBMIT PROPOSED SUBCONTRACTOR TO OWNER AND ARCHITECT FOR APPROVAL.
- PAINT COLOR TO BE CUSTOM TO MATCH SPECIFIED COLOR
- ALL WORK MUST BE COORDINATED WITH LANDLORD.
- FACE CLEAN, WET SAND AND SOLVENT WIPE ALL SURFACES TO BE PAINTED. APPLY PAINT IN THREE 1 MIL. COATS.
- ANY DISCREPANCY TO BE REMOVED FROM ADJACENT SURFACES




SEALANTS & MEMBRANES

- SEALANTS SHALL BE USED ONLY AS RECOMMENDED BY THE SEALANT MANUFACTURER FOR THE INTENDED USE.
- SUBMIT ALL SEALANT SPECIFICATIONS AND COLORS TO ARCHITECT FOR APPROVAL PRIOR TO PROCEEDING.
- ALL SEALANT JOINTS TO BE SMOOTH AND RECESSED UNLESS OTHERWISE INDICATED. NO SEALANT SHALL EXTEND OUTSIDE OF THE JOINT.
- SEALANT BETWEEN METAL PANELS SHALL MATCH THE COLOR OF THE ALUMINUM PANELS.
- SEALANT TOUCHING A FIELD PAINTED SURFACE SHALL BE PAINTABLE TYPE.
- SEALANT JOINTS SHALL BE 1/4" WIDE UNLESS OTHERWISE NOTED.
- SEALANT JOINT WIDTH AND DEPTH SHALL BE PER MANUFACTURERS' PARAMETERS. PROVIDE BACKER RODS.
- SEE SPECS FOR SEALANTS, MEMBRANES, & BUILDING WRAP.

SIGNAGE & AWNINGS

- REFER TO SIGNAGE & AWNING SHOP DRAWINGS FOR MORE INFORMATION.

Legend		
	Caulking	277.36
	Electrostatic Paint on Storefront Cladding	259.82
	Flashing	129.91
	Flashing	197.95
	Length Measurement	41.68
	Paint on Wall As PNT-1	751.8
	Stucco Finish on Wall	2,973.6
	Stucco Finish on Wall	296.44

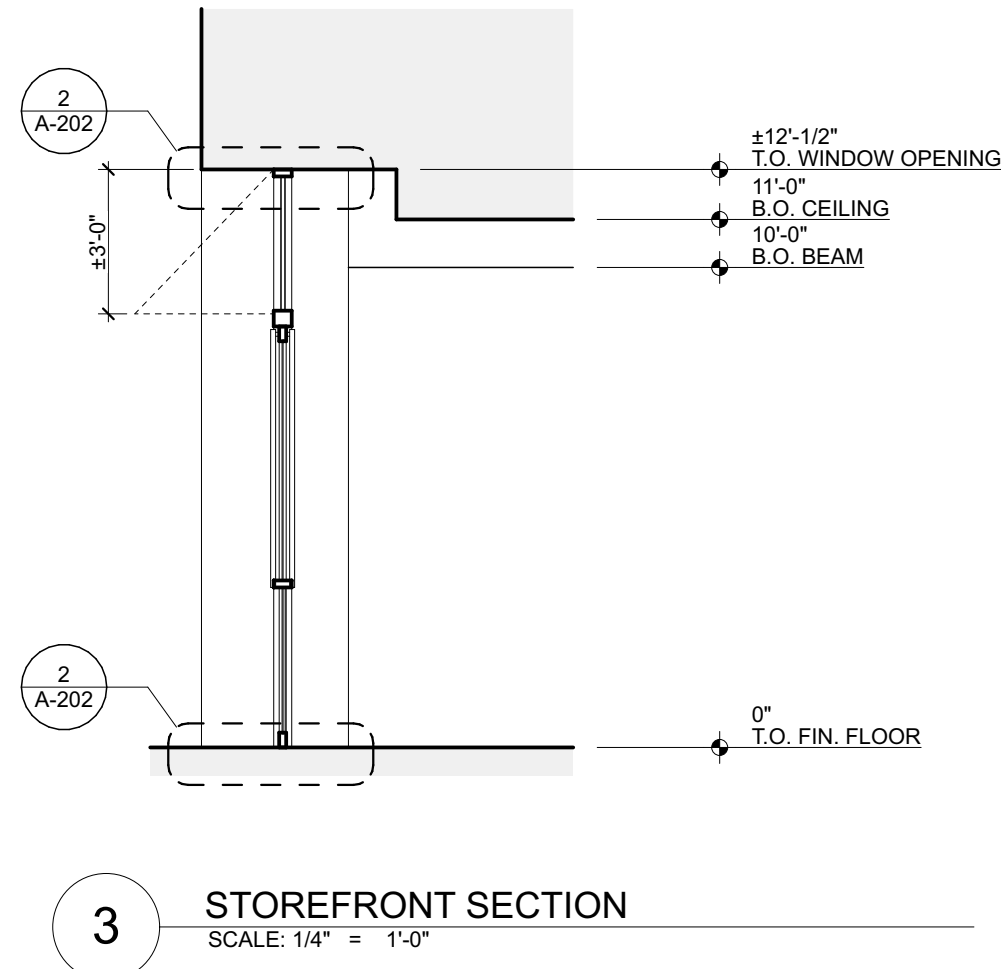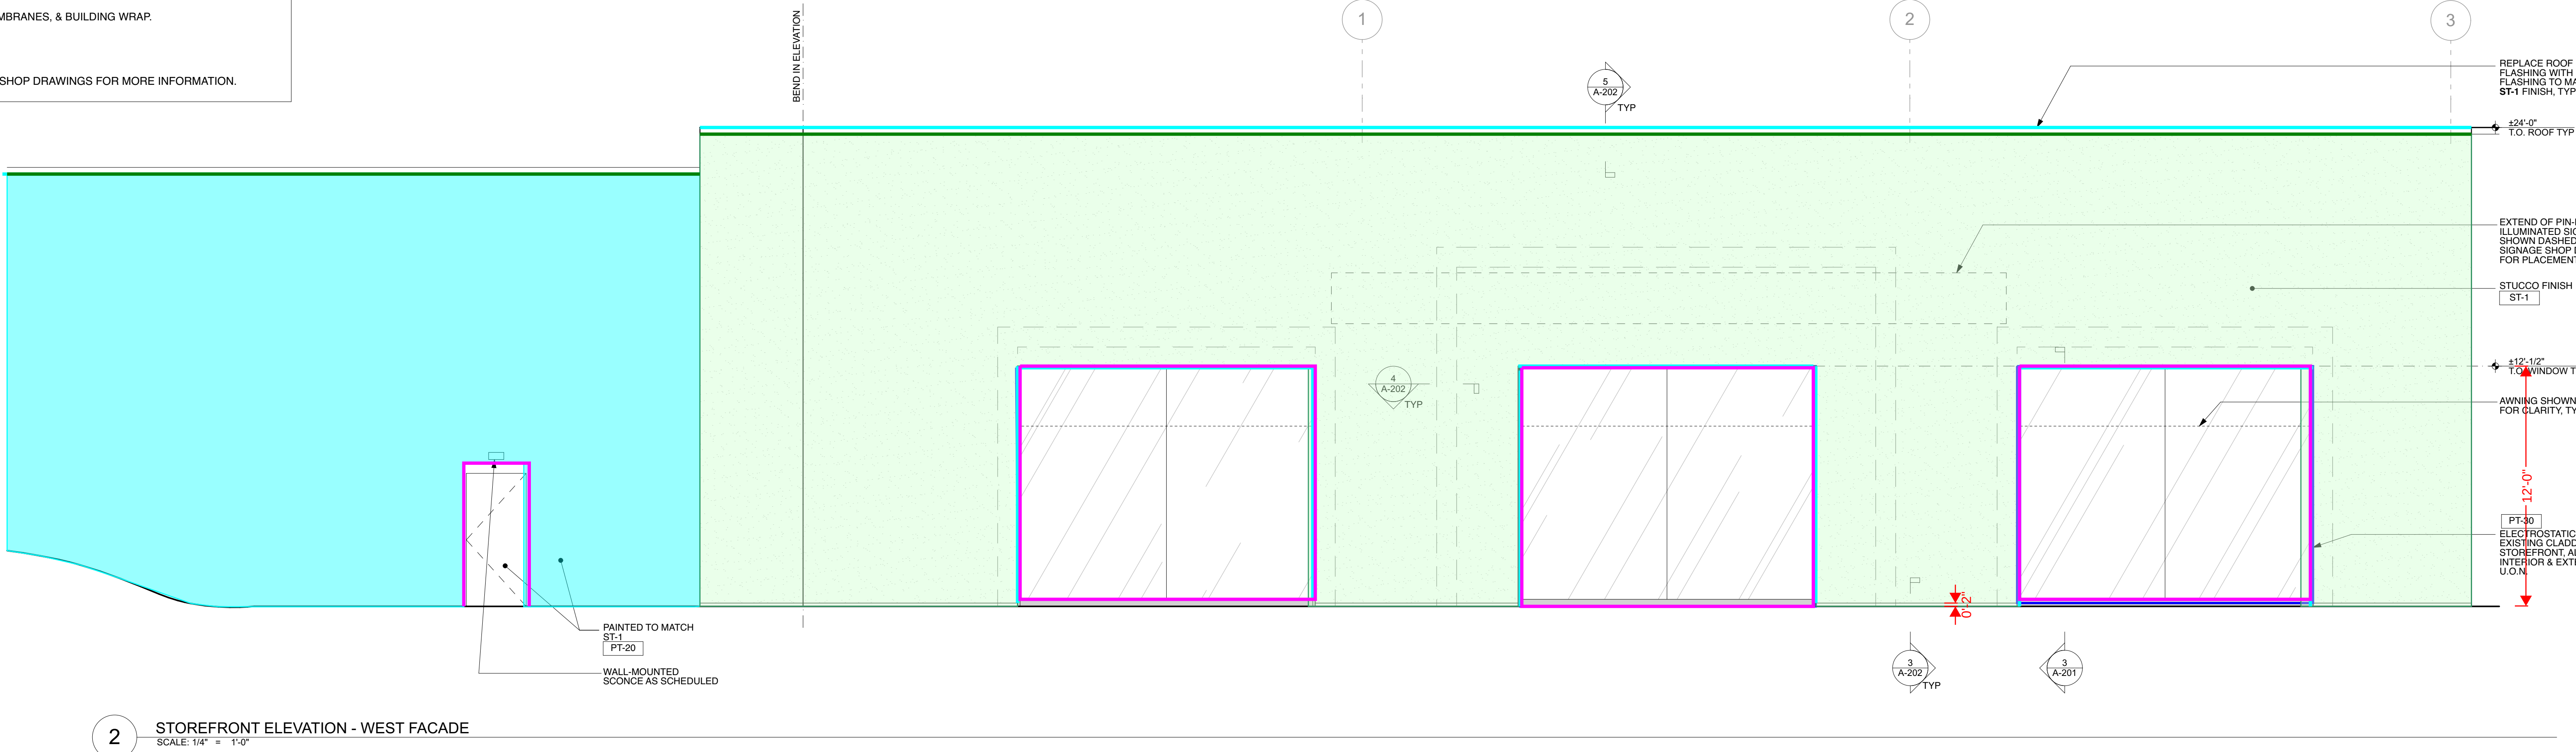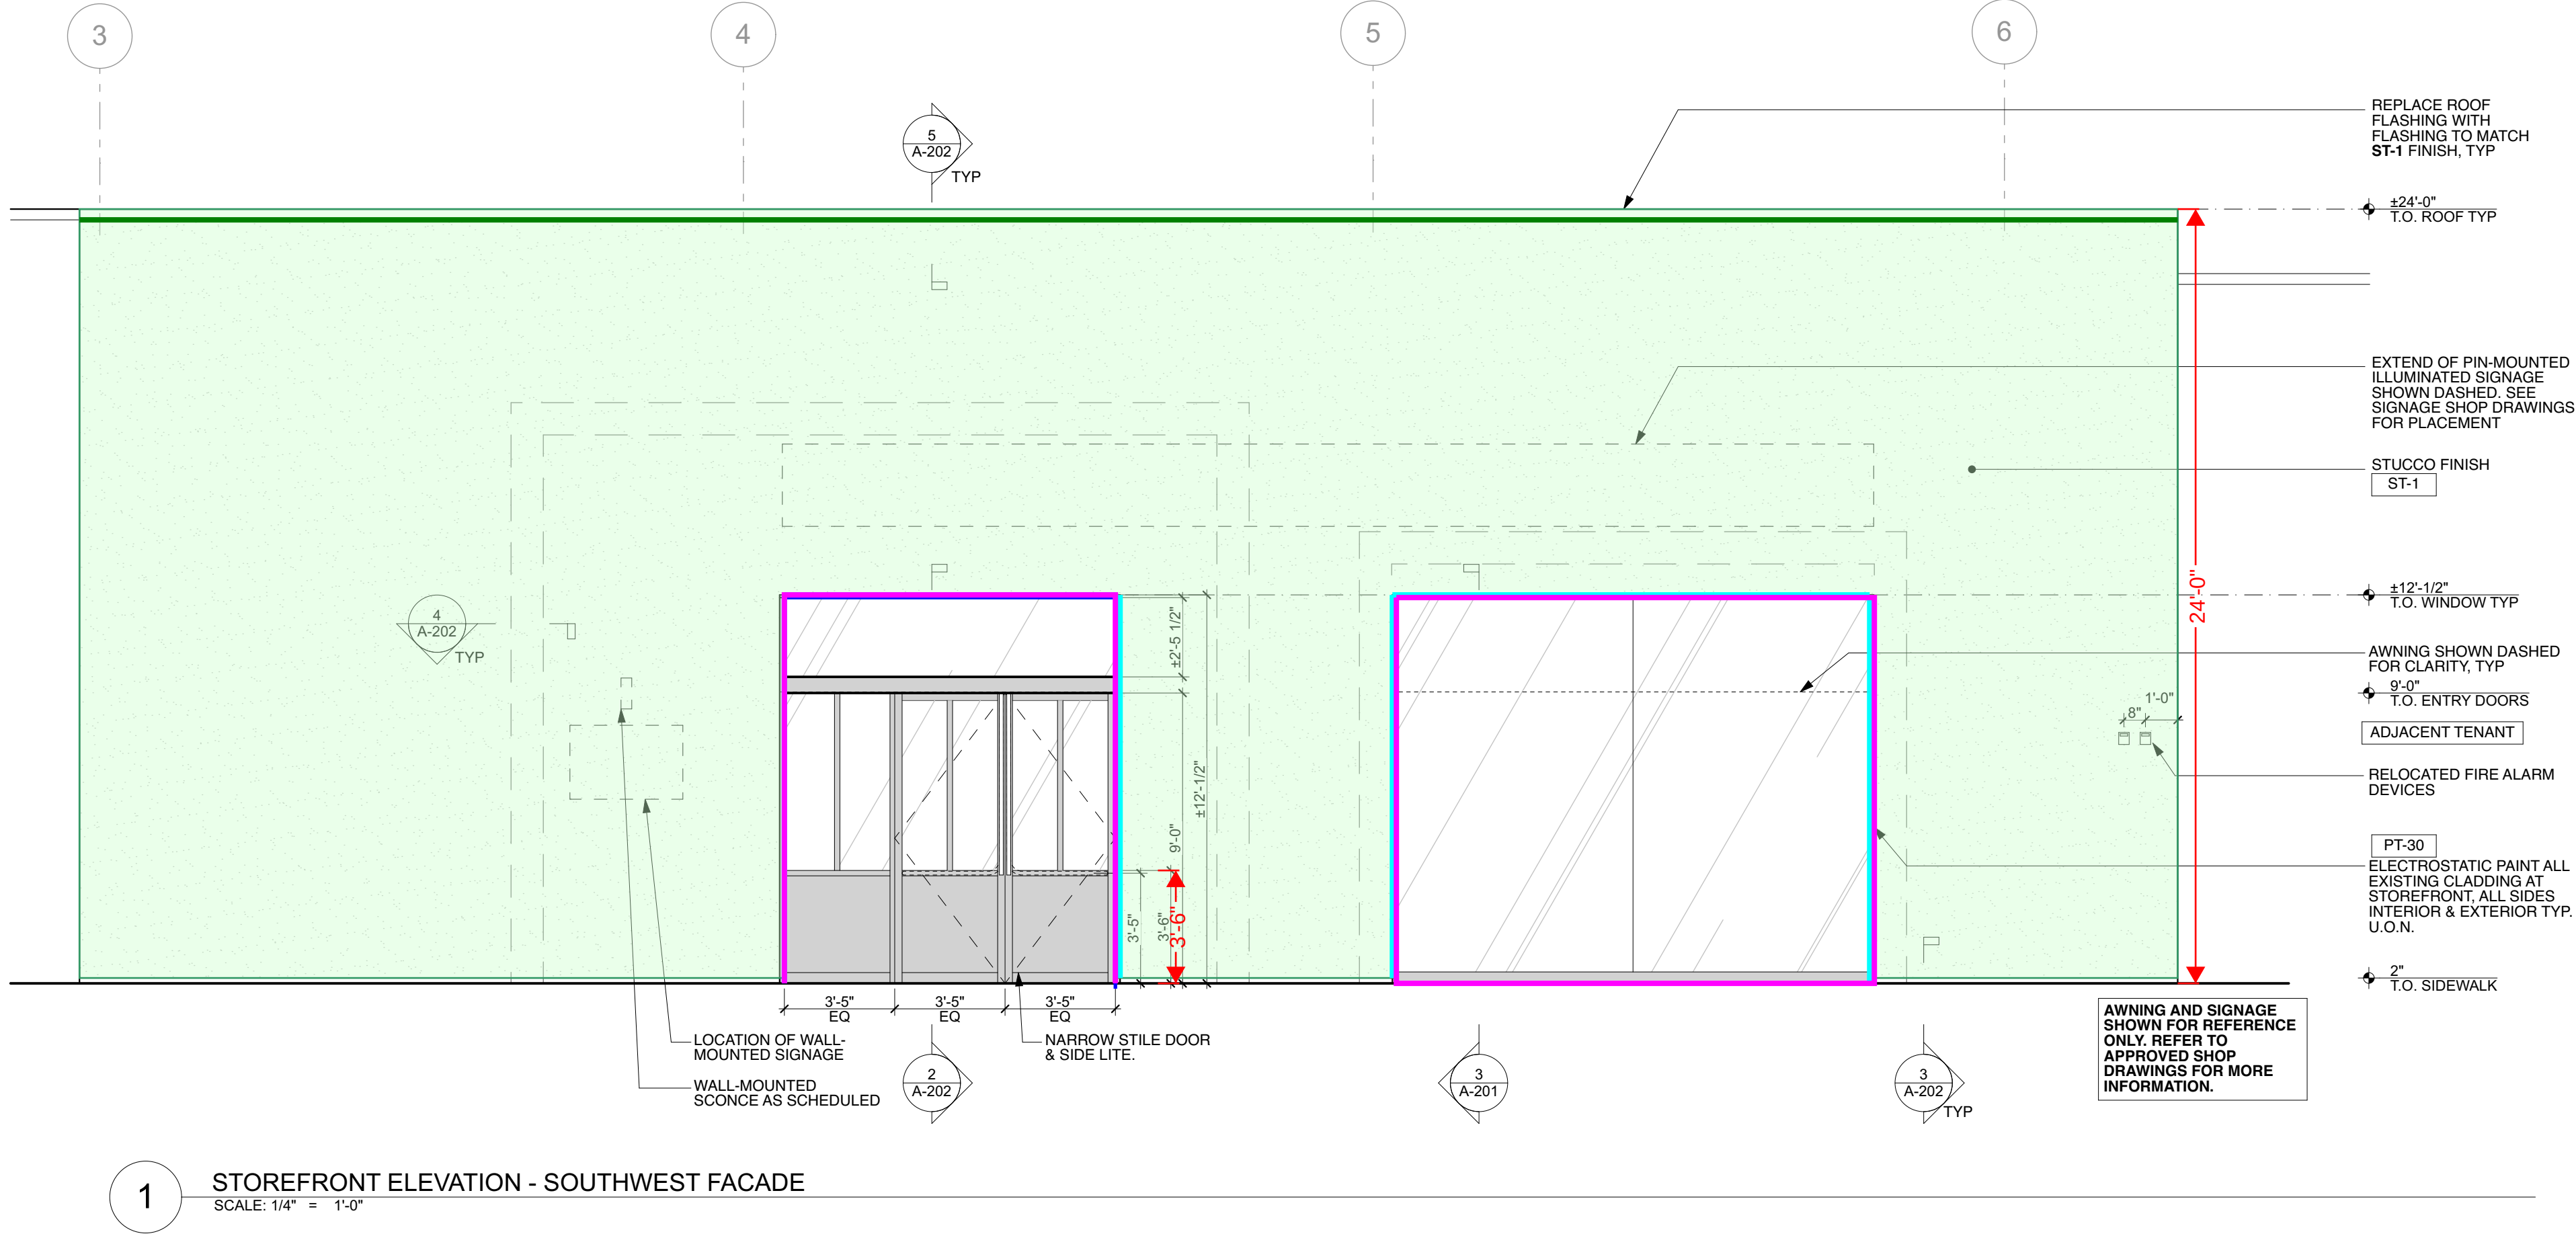

Lalire March Architects LLP
630 9th Avenue, Suite 900
New York New York 10036
212 807 1011

LalireMarchArchitects

NOT FOR
CONSTRUCTION

07.26.24	Issue for LL Review	
01.29.24	Issue for Bid	
	Survey Package	
NO.	DATE	ISSUE

Design Within Reach
776 Route 17 N
Unit 1A, Ground Level
Paramus, NJ 07652

LMA PROJECT NO. 24004

STOREFRONT
ELEVATION AND
SECTIONS

A-201